


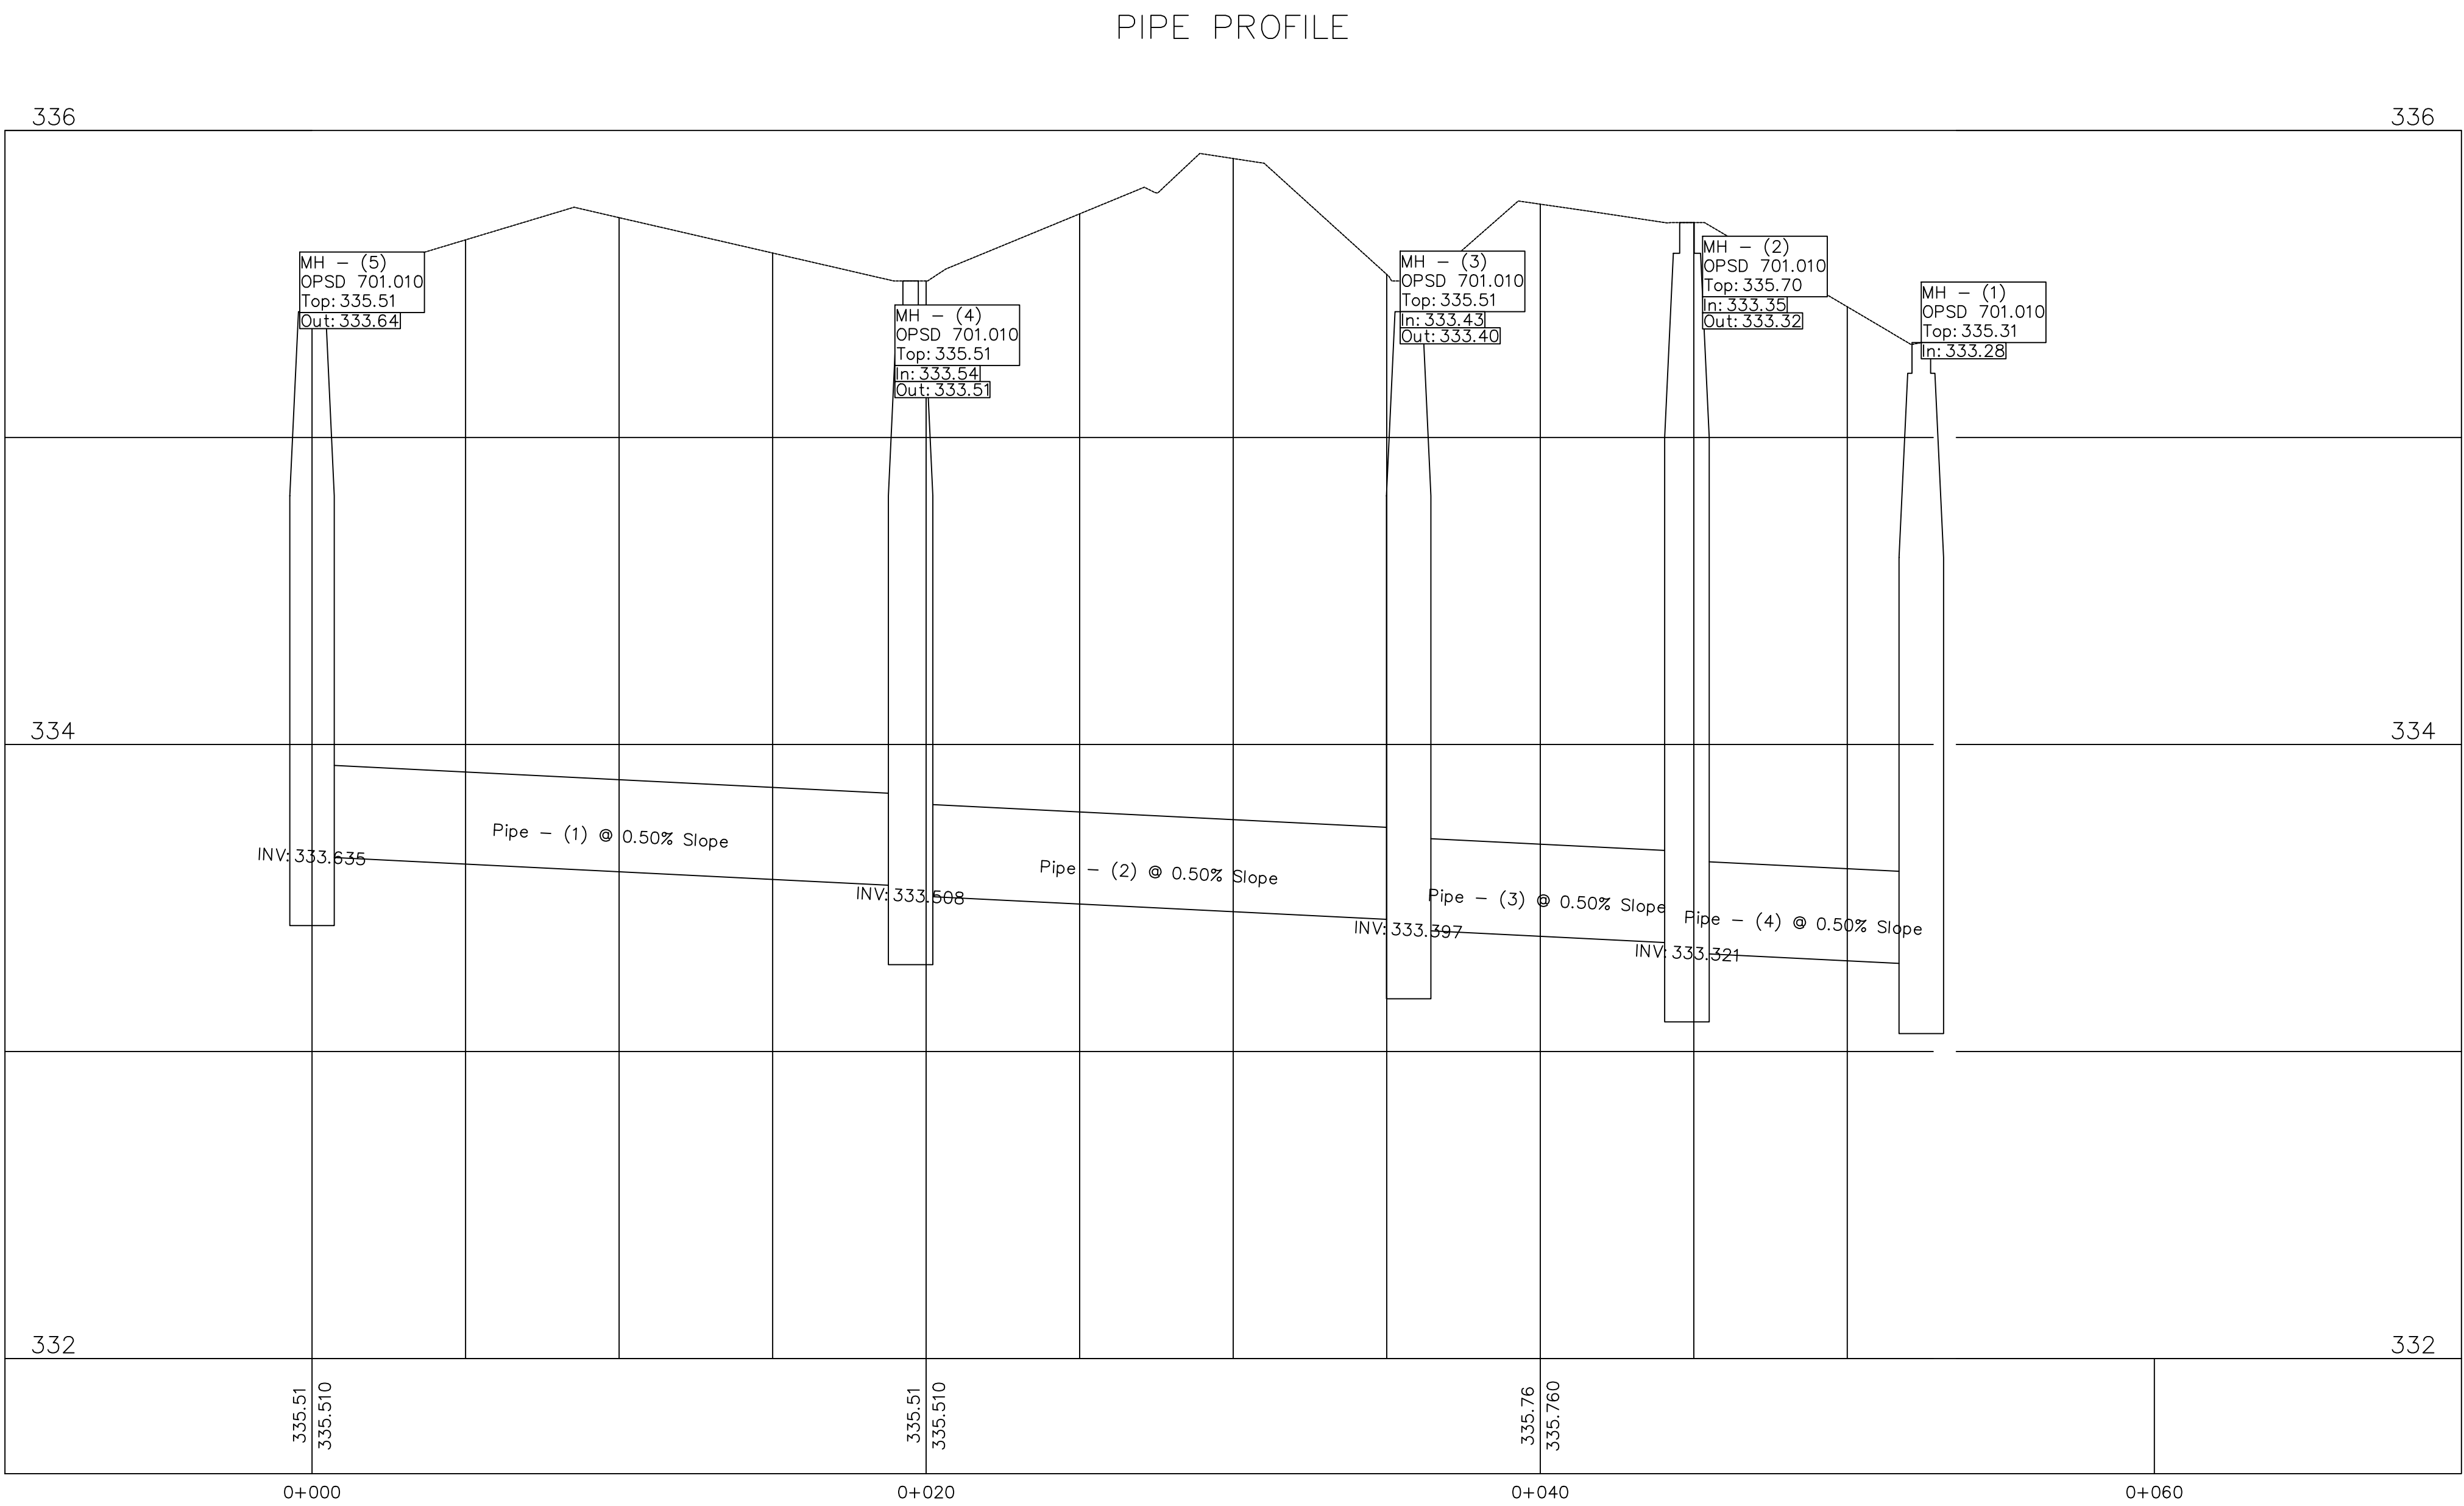

INIT	DATE	REVISIONS
CONSULTANT NAME		
Title		
Pipe_Profile		
DATE: August 12, 2026		DESIGN BY: AP
Scale: 1:150		DRWAN BY: AP
		CHECKED BY:
		Sheet Numer:
		3